BOU

ivia De Me

RLA


SCH

OOL



BOURLASCHOOL

Olivia De Mey

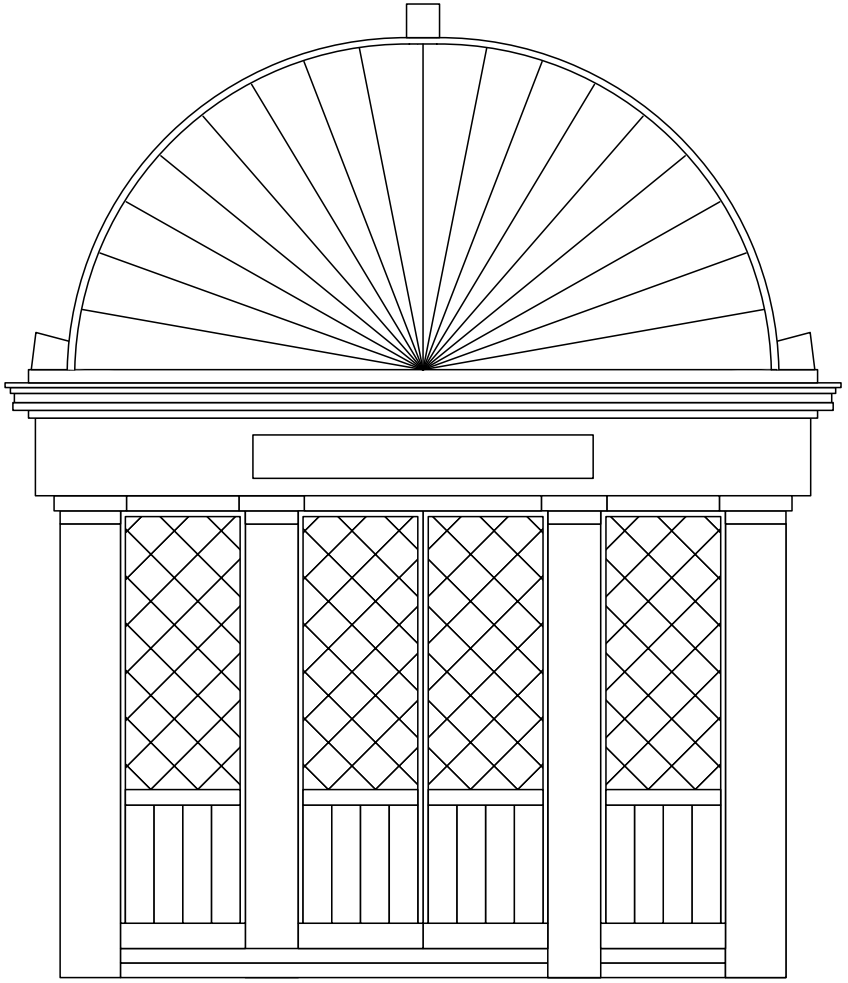

BOURLASCHOOL

Olivia De Mey
2025-2026

“A building is not something you finish, it’s something you start.”
– Stewart Brand


Universiteit Antwerpen

Presentatieportfolio
Copyright © 2026 door Olivia De Mey
lettertype: Myriad Pro
papier: Rebello

Universiteit Antwerpen, Campus Mutsaard
Mutsaardstraat 31, B-2000 Antwerpen
Tel. +32 3 265 41 11
Fax. +32 3 265 44 20

Faculteit Ontwerpwetenschappen
Interieurarchitectuur 2025-2026
begeleider: Stefan Dhert

Olivia De Mey
Lindendreef 56, B-2920 Kalmthout
olivia.demey@outlook.com
Tel. +32 468 15 73 75
Januari 2026, Antwerpen

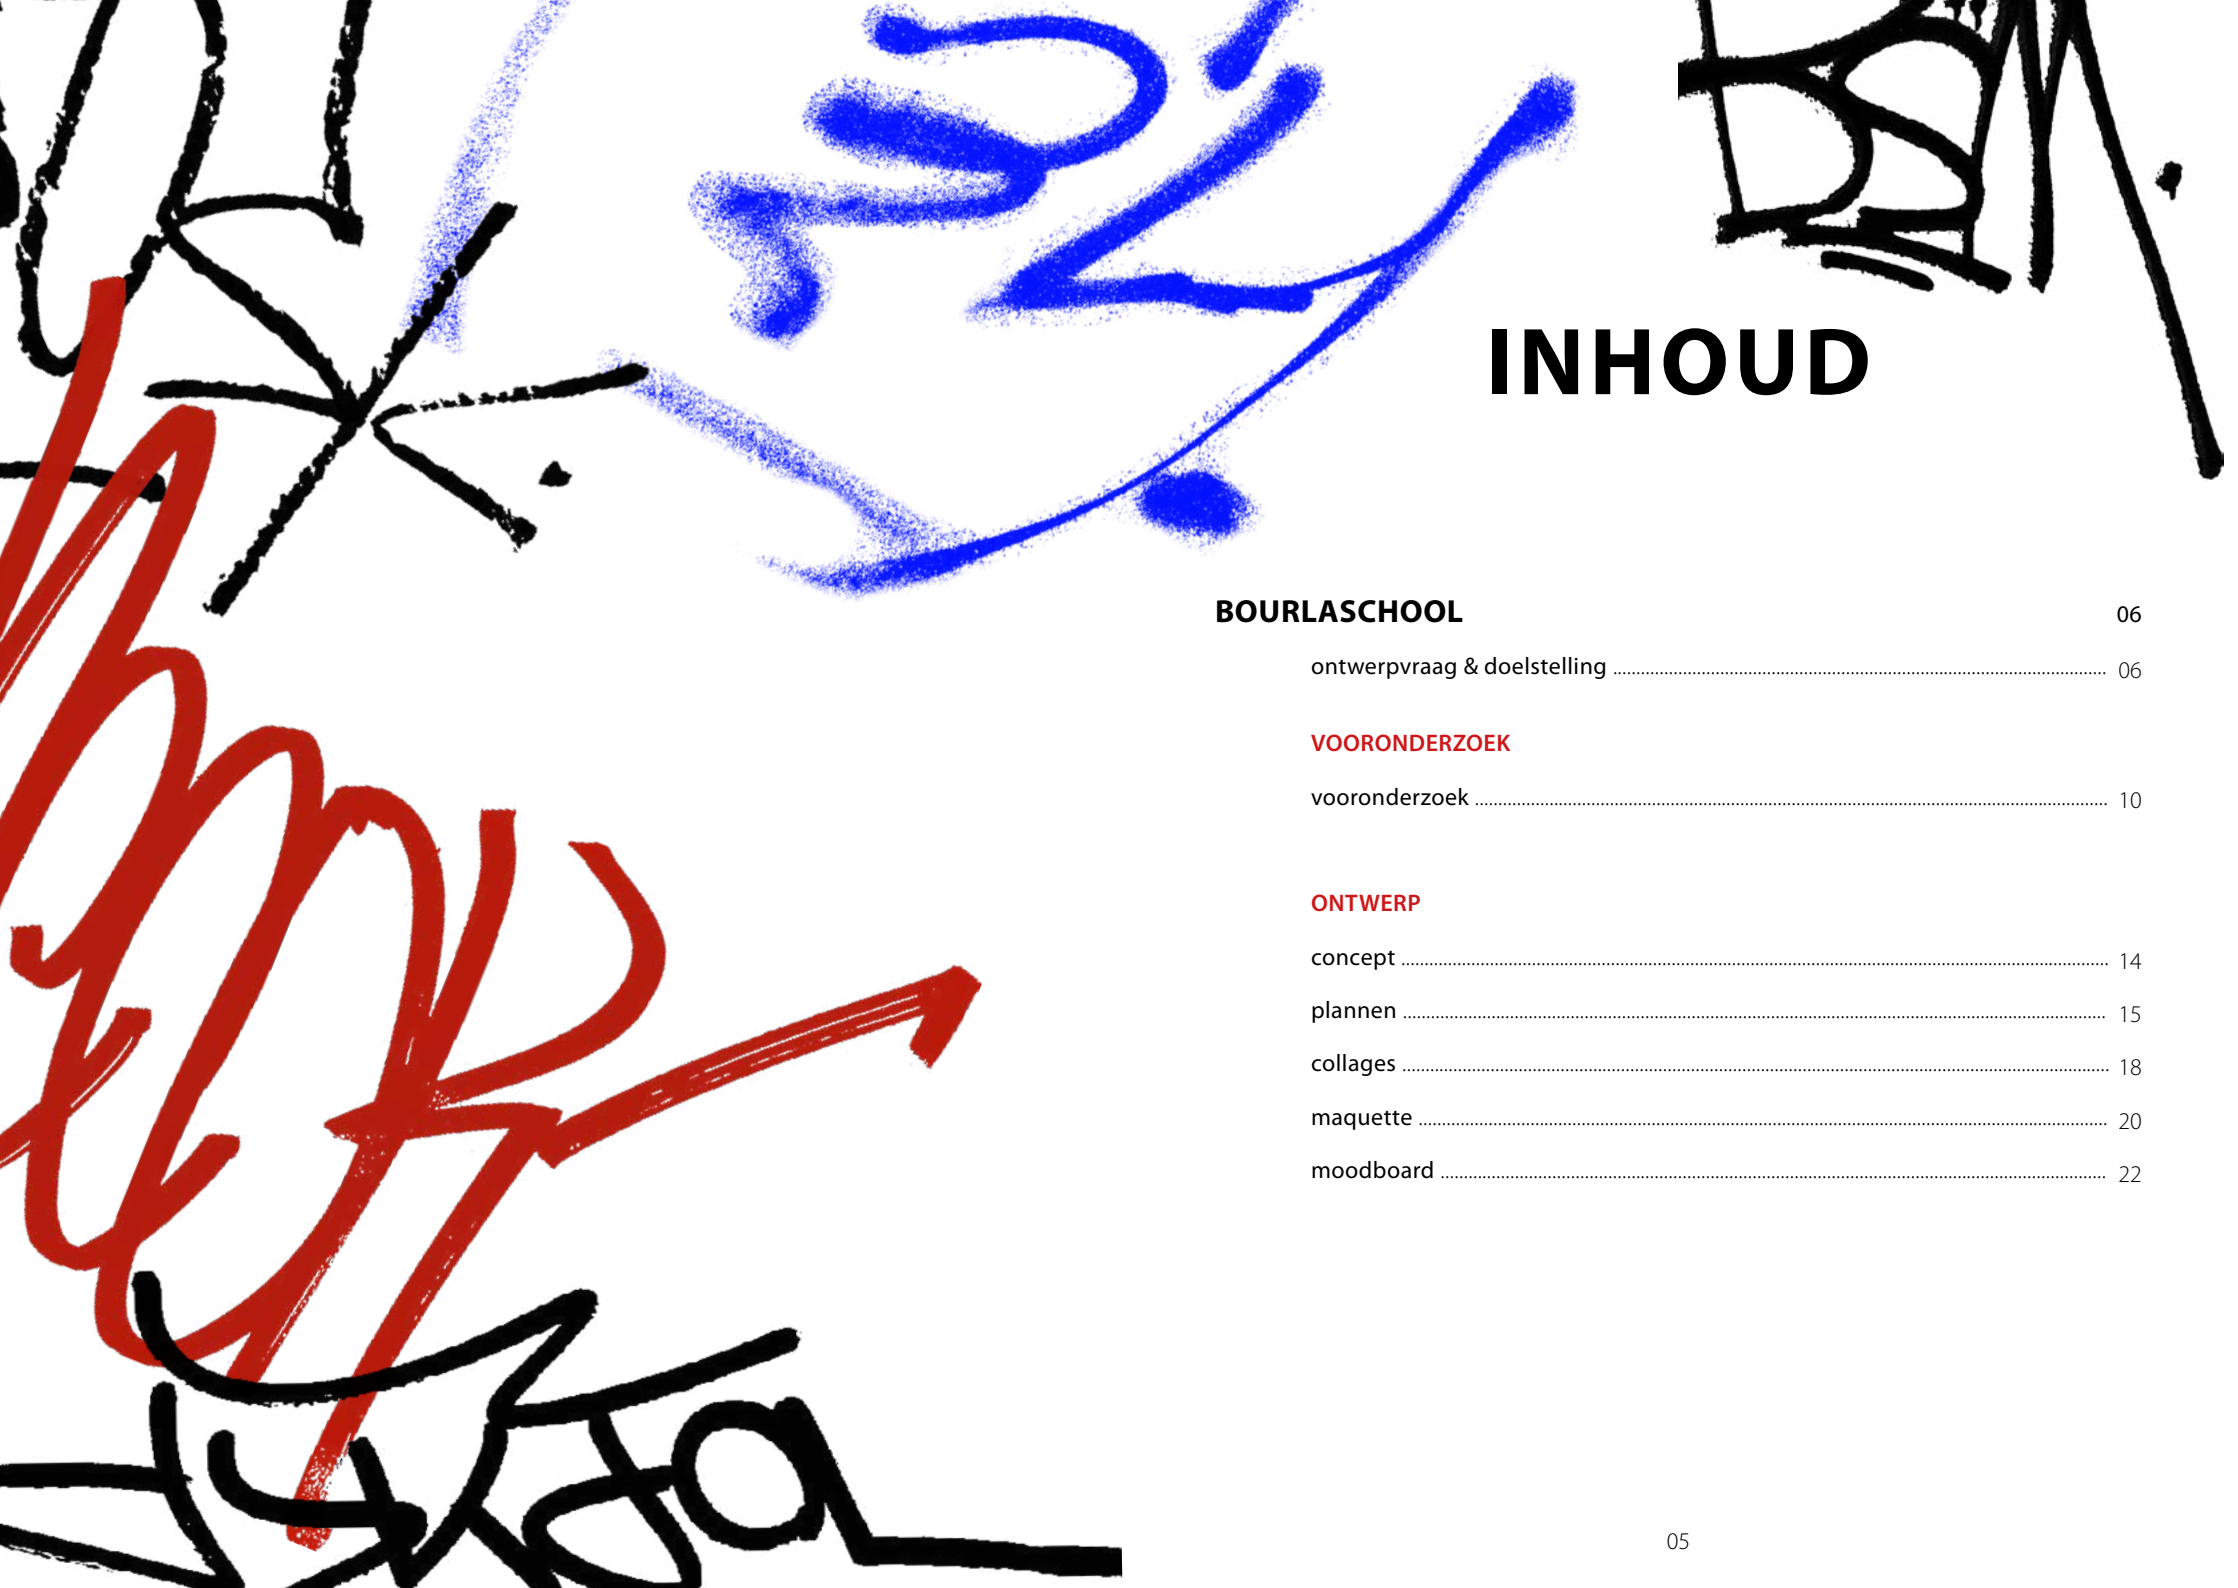

INHOUD

BOURLASCHOOL 06

ontwerpvraag & doelstelling 06

VOORONDERZOEK

vooronderzoek 10

ONTWERP

concept 14

plannen 15

collages 18

maquette 20

moodboard 22

BOURLASCHOOL

Ontwerpvraag & doelstelling

De herbestemming van de Bourlaschool vertrok vanuit de vraag: hoe kan het Bourla-gebouw worden ontworpen om een centraal ontmoetingspunt te vormen tussen twee scholen, rekening houdend met de bestaande context?
Hierbij ligt de focus op de ontmoeting tussen studenten van AP-hogeschool en Universiteit Antwerpen. De opleidingen op deze campus hebben een creatieve focus, die is doorgetrokken in dit ontwerp.
Een ander aandachtspunt is de bestaande context. Inzicht in de rijke geschiedenis, zorgt voor een respectvolle omgang met de omgeving en de materialen.



Graffiti op glas (Miyasaki, 2015)

VOOR-ONDER-ZOEK

-VOOR-
-ONDER-
ZOEK

Vooronderzoek



Het Bourla-gebouw is gebouwd in 1928. Het neoclassicistische gebouw heeft een lange, rechthoekige opbouw met een exterieur dat wordt gekenmerkt door bakstenen gevels en een uniek inkomsportaal. Binnenin is het gebouw opgedeeld in een inkomshal met een trap, een grote ruimte op het gelijkvloers en een grote ruimte op de eerste verdieping. Achteraan bevindt zich een aanbouw met een tweede trap en sanitaire voorzieningen. Aan de noordkant bevindt zich een grote serre, ingesloten door drie gevels. Op de eerste verdieping valt de dakstructuur, met houten spanten meteen op. Dit zorgt voor een zeer verschillend beeld vanop het gelijkvloers en de eerste verdieping. De bepleisterde binnenwanden creëeren een sterk contrast tussen de afgewerkte binnenmuren en ruwe buitenmuren.

Campus Mutsaard biedt veel kunst- en creatieve richtingen. De studenten zijn dan ook creatievelingen met een passie voor kunst. De gebouwen op deze campus weerspiegelen deze creatieve geest. Er zijn bijvoorbeeld doorheen de campus beelden geëxposeerd, in de cafetaria zal je tal van posters zien hangen, en zelfs als je de toiletten binnenstapt zie je graffiti. Ook in het Bourla-gebouw vallen de tekeningen en posters op de wanden op. De studenten hebben hun eigen manier gevonden om de gebouwen toe te eigenen: met kunst.

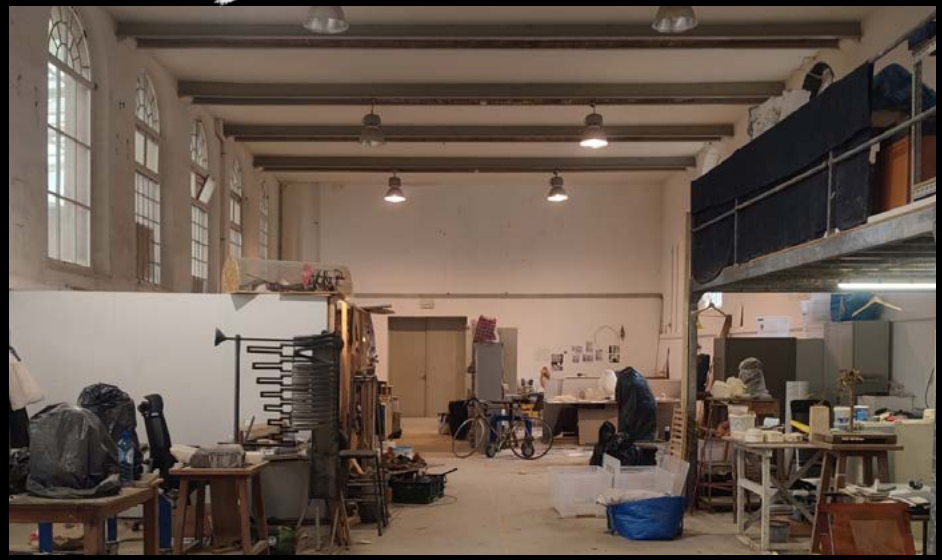


foto gelijkvloers


GESCHIEDENIS


1450: vestigen van Minderbroeders
1566: beeldenstorm
1794: Franse bezetting
1794: Minderbroeders verlaten klooster
1802: Bureel van Weldadigheid: opleiding conservatie-restauratie
1811: Koninklijke Academie voor Schone Kunsten
1819: stedelijk lager onderwijs
1928-1930: bouw Armenschool (Bourlaschool)
1830-1833: militaire inbeslagname (ziekenhuis)
1833: opening school
1842-1850: aanpassingen (compartimentalisering, 2e bouwlaag)
2010: restauratie
2012-heden: atelier ruimte: beeldhouwkunst







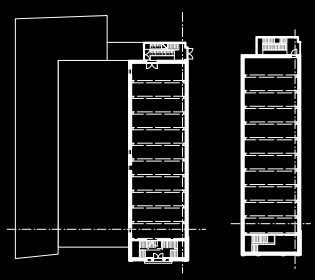

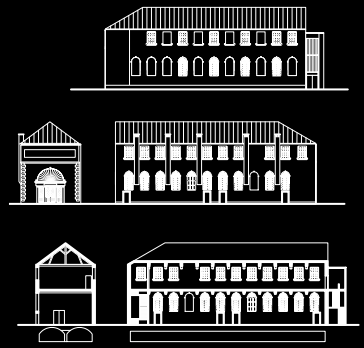

LIGGING

De bourlaschool is gelegen op de campus Mutsaard, in het centrum van Antwerpen. Door zijn centrale ligging is het makkelijk te bereiken met openbaar vervoer (trein, tram, bus, deelfiets).



poster site analyse

ONTWERP

ONTWERP

Concept

Dit project is 'van, voor en door studenten'. Dit betekent dat het een plek moet zijn waar studenten voelen dat de plaats van hen is, een plek die ze kunnen toe-eigenen. Door verschillende ingrepen wordt het een plaats 'door' studenten, waarbij studenten actief kunnen bijdragen. Dit is mogelijk door twee 'graffiti volumes' centraal te plaatsen, waarop studenten kunnen schrijven en/of tekenen. Graffiti is een rebelse vorm van zelfexpressie die historisch belangrijk was om een stem te geven aan wie anders niet gehoord werd. De mogelijkheid om op muren te schrijven en tekenen geeft studenten die stem.
Centraal in het gebouw is er een vide die over de volledige hoogte van het gebouw loopt. Het is ruimte voor een kunstinstallatie die studenten zelf ontwerpen.
Doorheen het gebouw komen er tweedehandse, gerecycleerde, en/of zelfgemaakte meubels (door studenten).






Graffiti (Brugnoli, z.d.)
Belang van graffiti (Kemp, 1972)


Plannen

schaal 1:300

GRONDPLAN GELIJKVLOERS

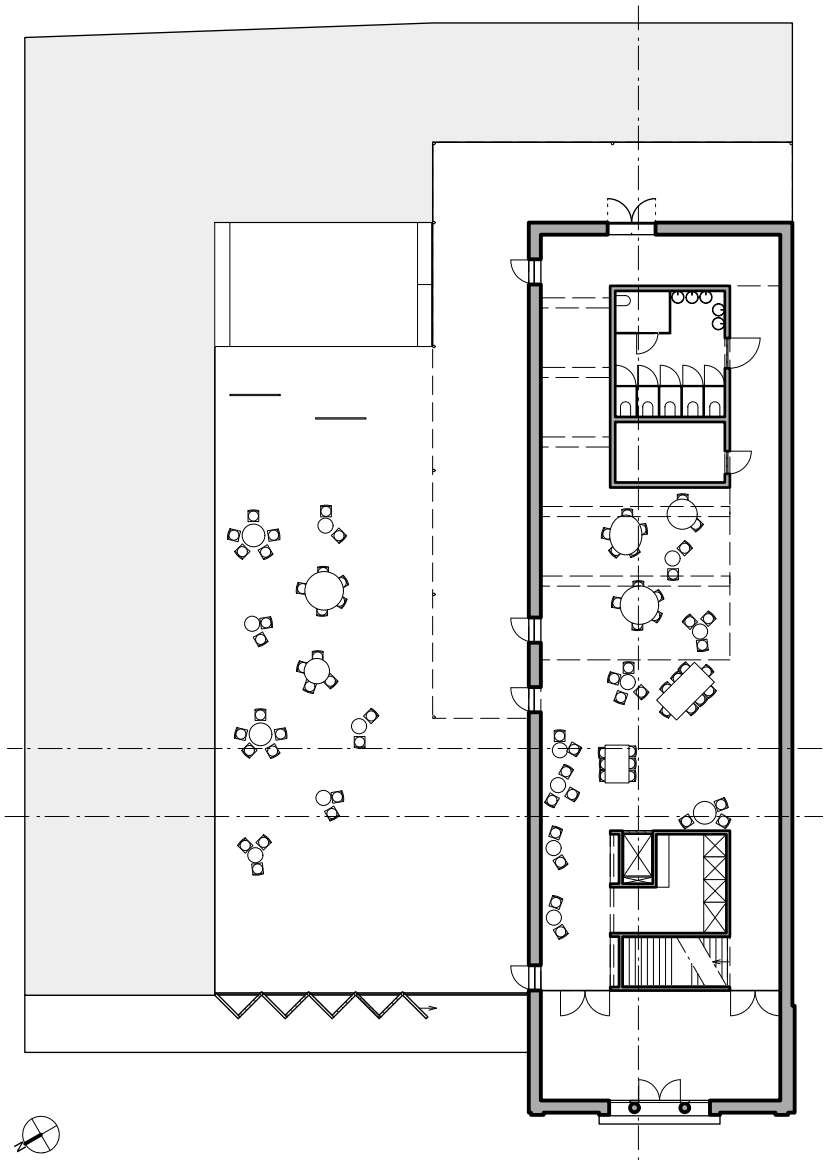



GRONDPLAN 1E VERDIEP

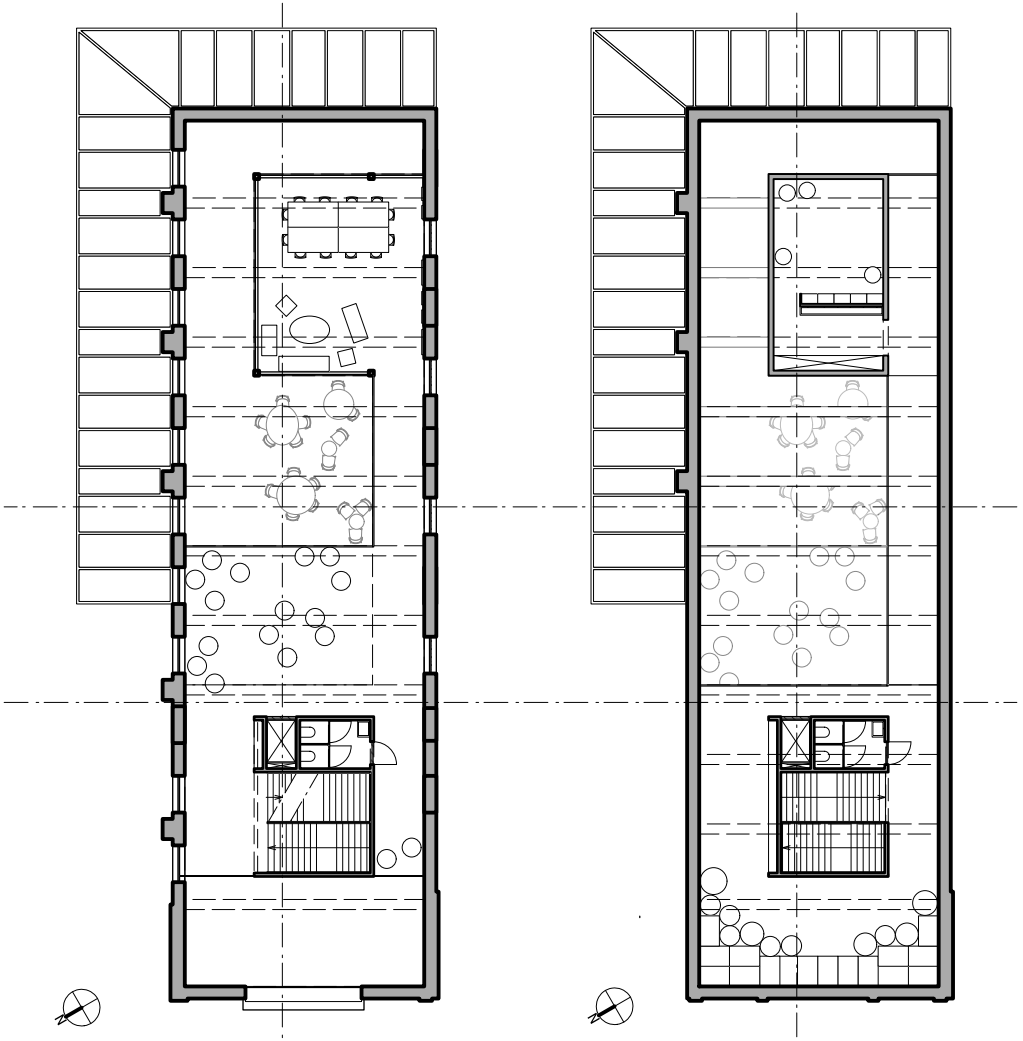

GRONDPLAN 2E VERDIEP

SNEDES

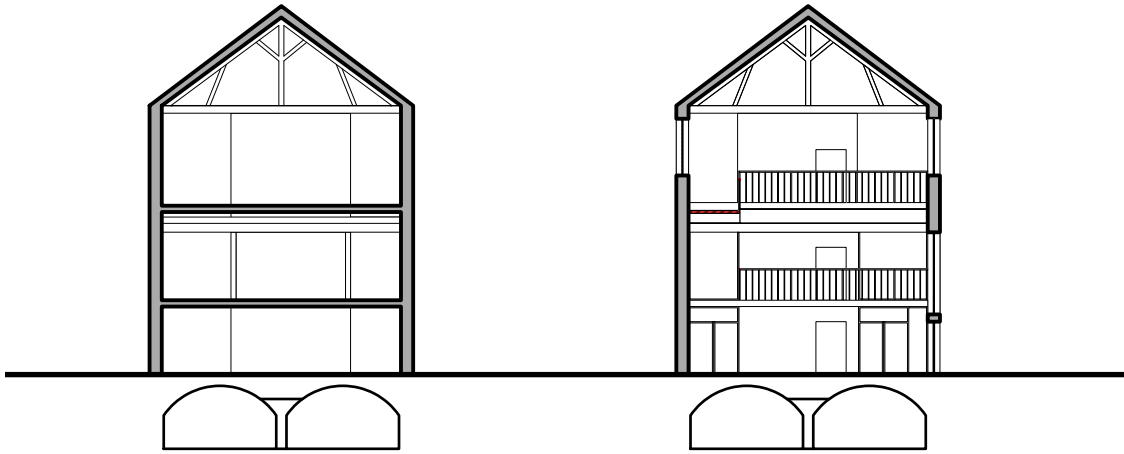

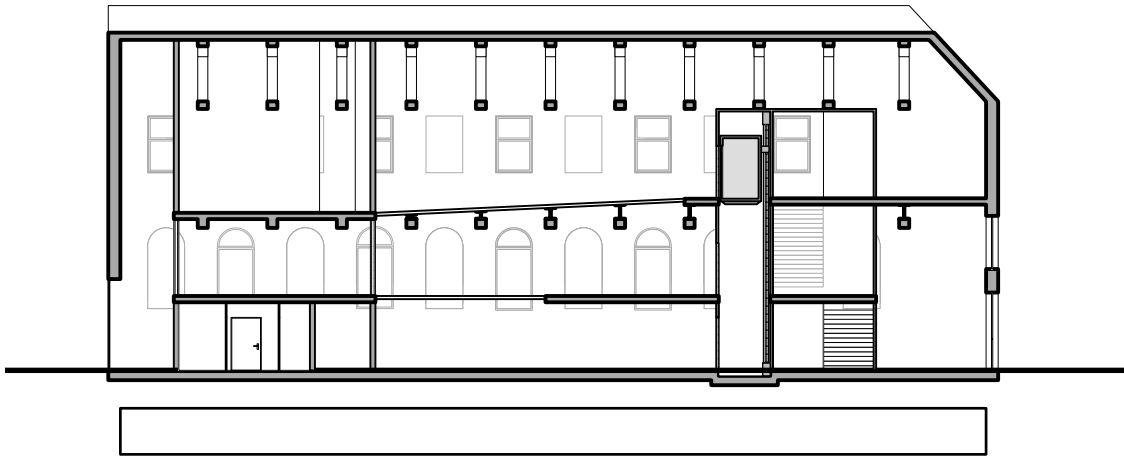

Collages



collage



collage

Maquette





foto maquette loopbrug
foto maquette interieur 1e verdieping



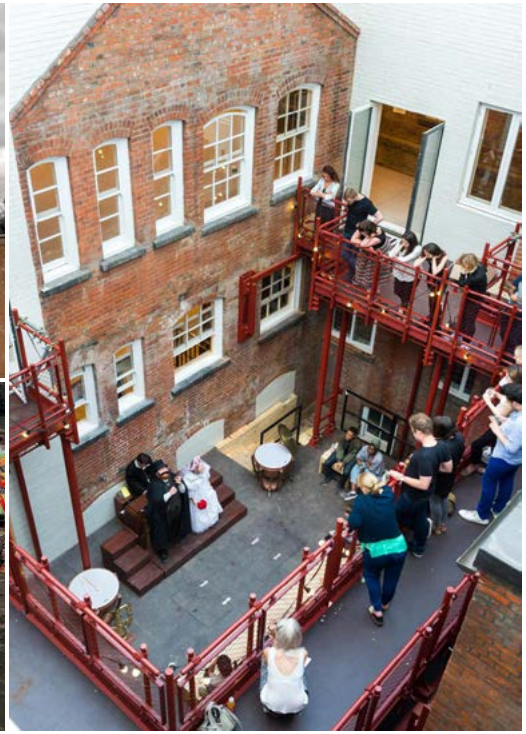


foto maquette aanzicht
foto maquette exterieur

Moodboard












Skate Ramp (Tornberg, z.d.)
Gerecycleerde Meubels (Scott, 2025)
Expositie (Sze, 2017)

Loopbrug (Brenner, 2017)
Graffiti (Vidriera, z.d.)



OLIVIA DE MEY

Olivia De Mey (2006) volgt momenteel de tweede bachelor interieurarchitectuur aan de Universiteit Antwerpen. Ze gunt zichzelf de ruimte om op zoek te gaan naar haar identiteit als ontwerper. Dit zorgt voor een experimenteel ontwerpproces met ruimte voor ontdekking. Haar creativiteit wordt geprikkeld door veel uiteenlopende interesses: kunst, muziek, menselijke interacties, ecologie. Ze is vooral geboeid door hoe ruimtes, ook na het ontwerpen, vorm krijgen door mensen. Deze interesses zorgen voor creatieve ontwerpen met een focus op gebruikers, omgeving en duurzaamheid.

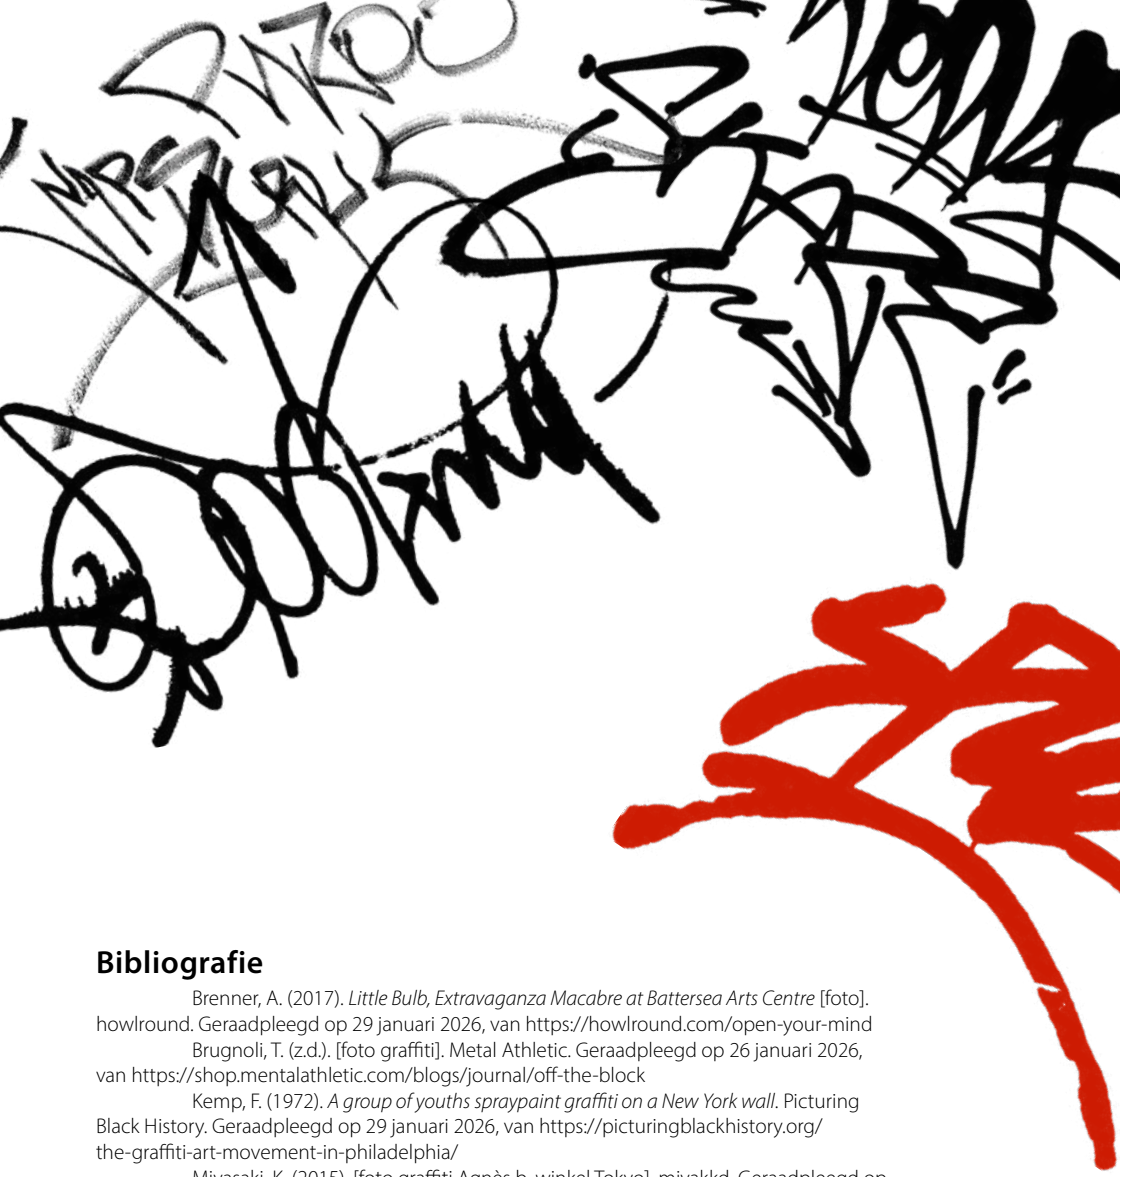

Bibliografie

Brenner, A. (2017). *Little Bulb, Extravaganza Macabre at Battersea Arts Centre* [foto]. howlround. Geraadpleegd op 29 januari 2026, van https://howlround.com/open-your-mind

Brugnoli, T. (z.d.). [foto graffiti]. Metal Athletic. Geraadpleegd op 26 januari 2026, van https://shop.mentalathletic.com/blogs/journal/off-the-block

Kemp, F. (1972). *A group of youths spraypaint graffiti on a New York wall*. Picturing Black History. Geraadpleegd op 29 januari 2026, van https://picturingblackhistory.org/the-graffiti-art-movement-in-philadelphia/

Miyasaki, K. (2015). [foto graffiti Agnès b. winkel Tokyo]. miyakkd. Geraadpleegd op 29 januari 2026, van https://miyakkd.com/?p=627

Scott, I. (2025). [foto Leake Street Arches]. Linkedin. Geraadpleegd op 29 januari 2026, van https://www.linkedin.com/posts/ian-scott-0534694-isrc-londonretail-activity-7399356928834818048-UlG3/

Sze, S. (2017). *Centrifuge* [foto]. hausderkunst. Geraadpleegd op 29 januari 2026, van https://www.hausderkunst.de/eintauchen/der-ffentlichkeit-von-den-freunden-haus-der-kunst-sarah-sze

Tornberg, T. (z.d.). *Skater on Edge of Skate Ramp* [foto]. pexels. Geraadpleegd op 29 januari 2026, van https://www.pexels.com/nl-nl/foto/skater-op-rand-van-skate-ramp-1587269/

Vidriera. (z.d.). [foto Bond Street Buenos Aires]. Galería Bond Street. Geraadpleegd op 29 januari 2026, van https://vidrierabuenosaires.com/lugares/bond-street